PROYECTO BÁSICO Y DE EJECUCIÓN

VIVIENDA UNIFAMILIAR EN PLANTA BAJA CON PATIO Y PISCINA + ESPACIO EN BRUTO EN PLANTA ALTA

Calle Moreno Torroba s/n · 14700 Palma del Río (Córdoba) | Ley 38/1999 (LOE) · R.D. 314/2006 (CTE)

TOMO II: ÁLBUM DE PLANOS REGLAMENTARIOS

Colección Completa de Láminas Técnicas Ejecutivas a Escalas Normalizadas (A3)


Aprobación de Licencia Urbanística de Obras · Visado Colegial COACo

ÍNDICE GENERAL DE LÁMINAS TÉCNICAS:

PLANO P-00	SITUACIÓN, EMPLAZAMIENTO Y JUSTIFICACIÓN PGOU (OCUPACIÓN 80% Y PATIO 40 m²)	**ESCALA 1:100**
PLANO P-01	PLANTA BAJA AMUEBLADA Y ACOTADA (MASTER SUITE, PATIO, PISCINA Y GARAJE)	**ESCALA 1:50**
PLANO P-02	PLANTA ALTA · ESPACIO DIÁFANO EN BRUTO SIN USO DEFINIDO Y PREINSTALACIONES	**ESCALA 1:50**
PLANO P-03	PLANTA DE CUBIERTAS E INSTALACIONES (XPS 100 mm, AEROTERMIA Y FOTOVOLTAICA)	**ESCALA 1:100**
PLANO P-04	ALZADOS EXTERIORES GENERALES (FACHADA SUR MORENO TORROBA Y FACHADA NORTE GARAJE)	**ESCALA 1:100**
PLANO P-05	SECCIONES CONSTRUCTIVAS LONGITUDINAL A-A' Y TRANSVERSAL B-B' (-1,50 m)	**ESCALA 1:75**
PLANO P-06	ESTRUCTURA, CIMENTACIÓN Y RED DE SANEAMIENTO ENTERRADA (HA-25 Y PVC Ø160)	**ESCALA 1:75**
PLANO P-07	INSTALACIONES GENERALES (CLIMATIZACIÓN B4, VMC DOBLE FLUJO, ELECTRICIDAD Y WALLBOX)	**ESCALA 1:75**

ARQUITECTO PROYECTISTA	DIRECCIÓN DE EJECUCIÓN	LA PROPIEDAD / PROMOTOR
Firma y Visado Colegial COACo	Arquitecto Técnico / Aparejador	Conforme con el Proyecto

VIAL PÚBLICO SECUNDARIO TRASERO (FACHADA NORTE · ACCESO RODADO COCHERA)

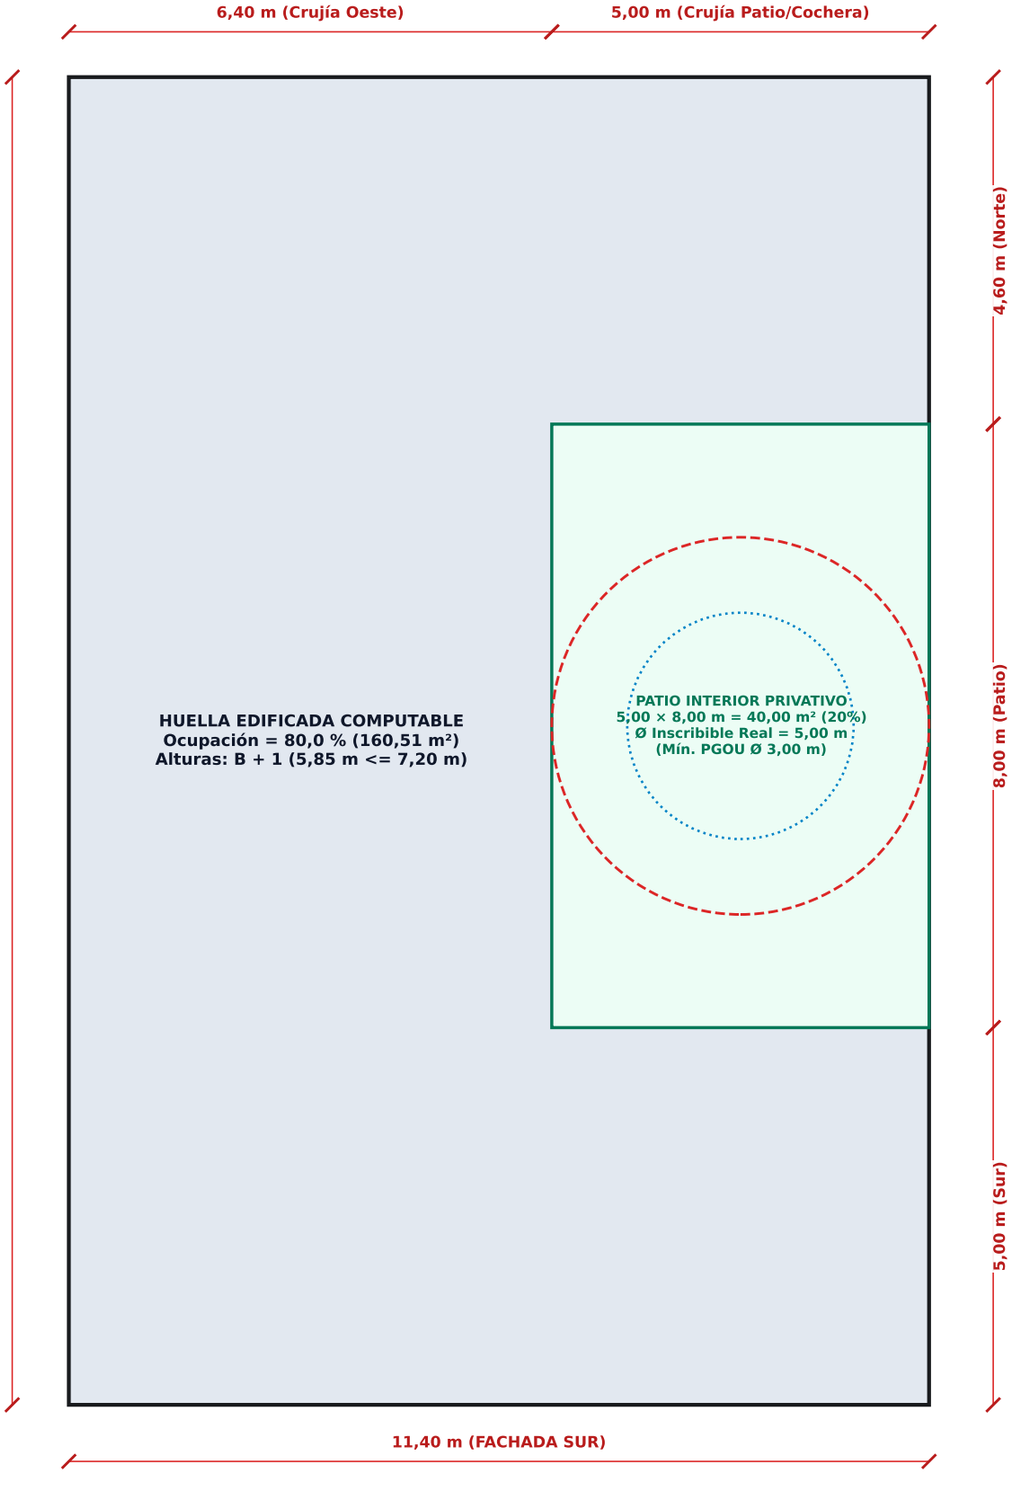


PARÁMETROS PGOU PALMA DEL RÍO

- Clasificación: Suelo Urbano Consolidado
- Uso Global: Residencial entre medianeras
- Solar: 11,40 × 17,60 m = 200,64 m²
- Ocupación Máx. PGOU: 80 % (160,51 m²)
- Ocupación Proyecto: 80,0 % (CUMPLE)
- Espacio Libre Patio: 40,13 m² (20,0 %)
- Diámetro Inscribible Patio: 5,00 m >= 3,00 m
- Altura Máx. Cornisa: 7,20 m (B+1)
- Altura Proyecto: 5,85 m (B+1) (CUMPLE)
- Modalidad: PB Terminada + PA en Bruto
- Aparcamiento: 1 Plaza en PB (21,14 m²)

CALLE MORENO TORROBA (FACHADA PRINCIPAL SUR · ACCESO PEATONAL)

PROYECTO BÁSICO Y DE EJECUCIÓN Vivienda Unifamiliar en PB + Espacio en Bruto en PA **Calle Moreno Torroba s/n · Palma del Río (Córdoba)**	**PLANO: EMPLAZAMIENTO, PARCELA Y JUSTIFICACIÓN PGOU** Alineaciones, Ocupación en Planta (80%), Patio Central y Cuadro Urbanístico **Documento Reglamentario CTE · Solicitud Licencia de Obras**	**ESCALA: 1:100** FECHA: Octubre 2026 FORMATO: DIN A3	PLANO Nº **P-00**

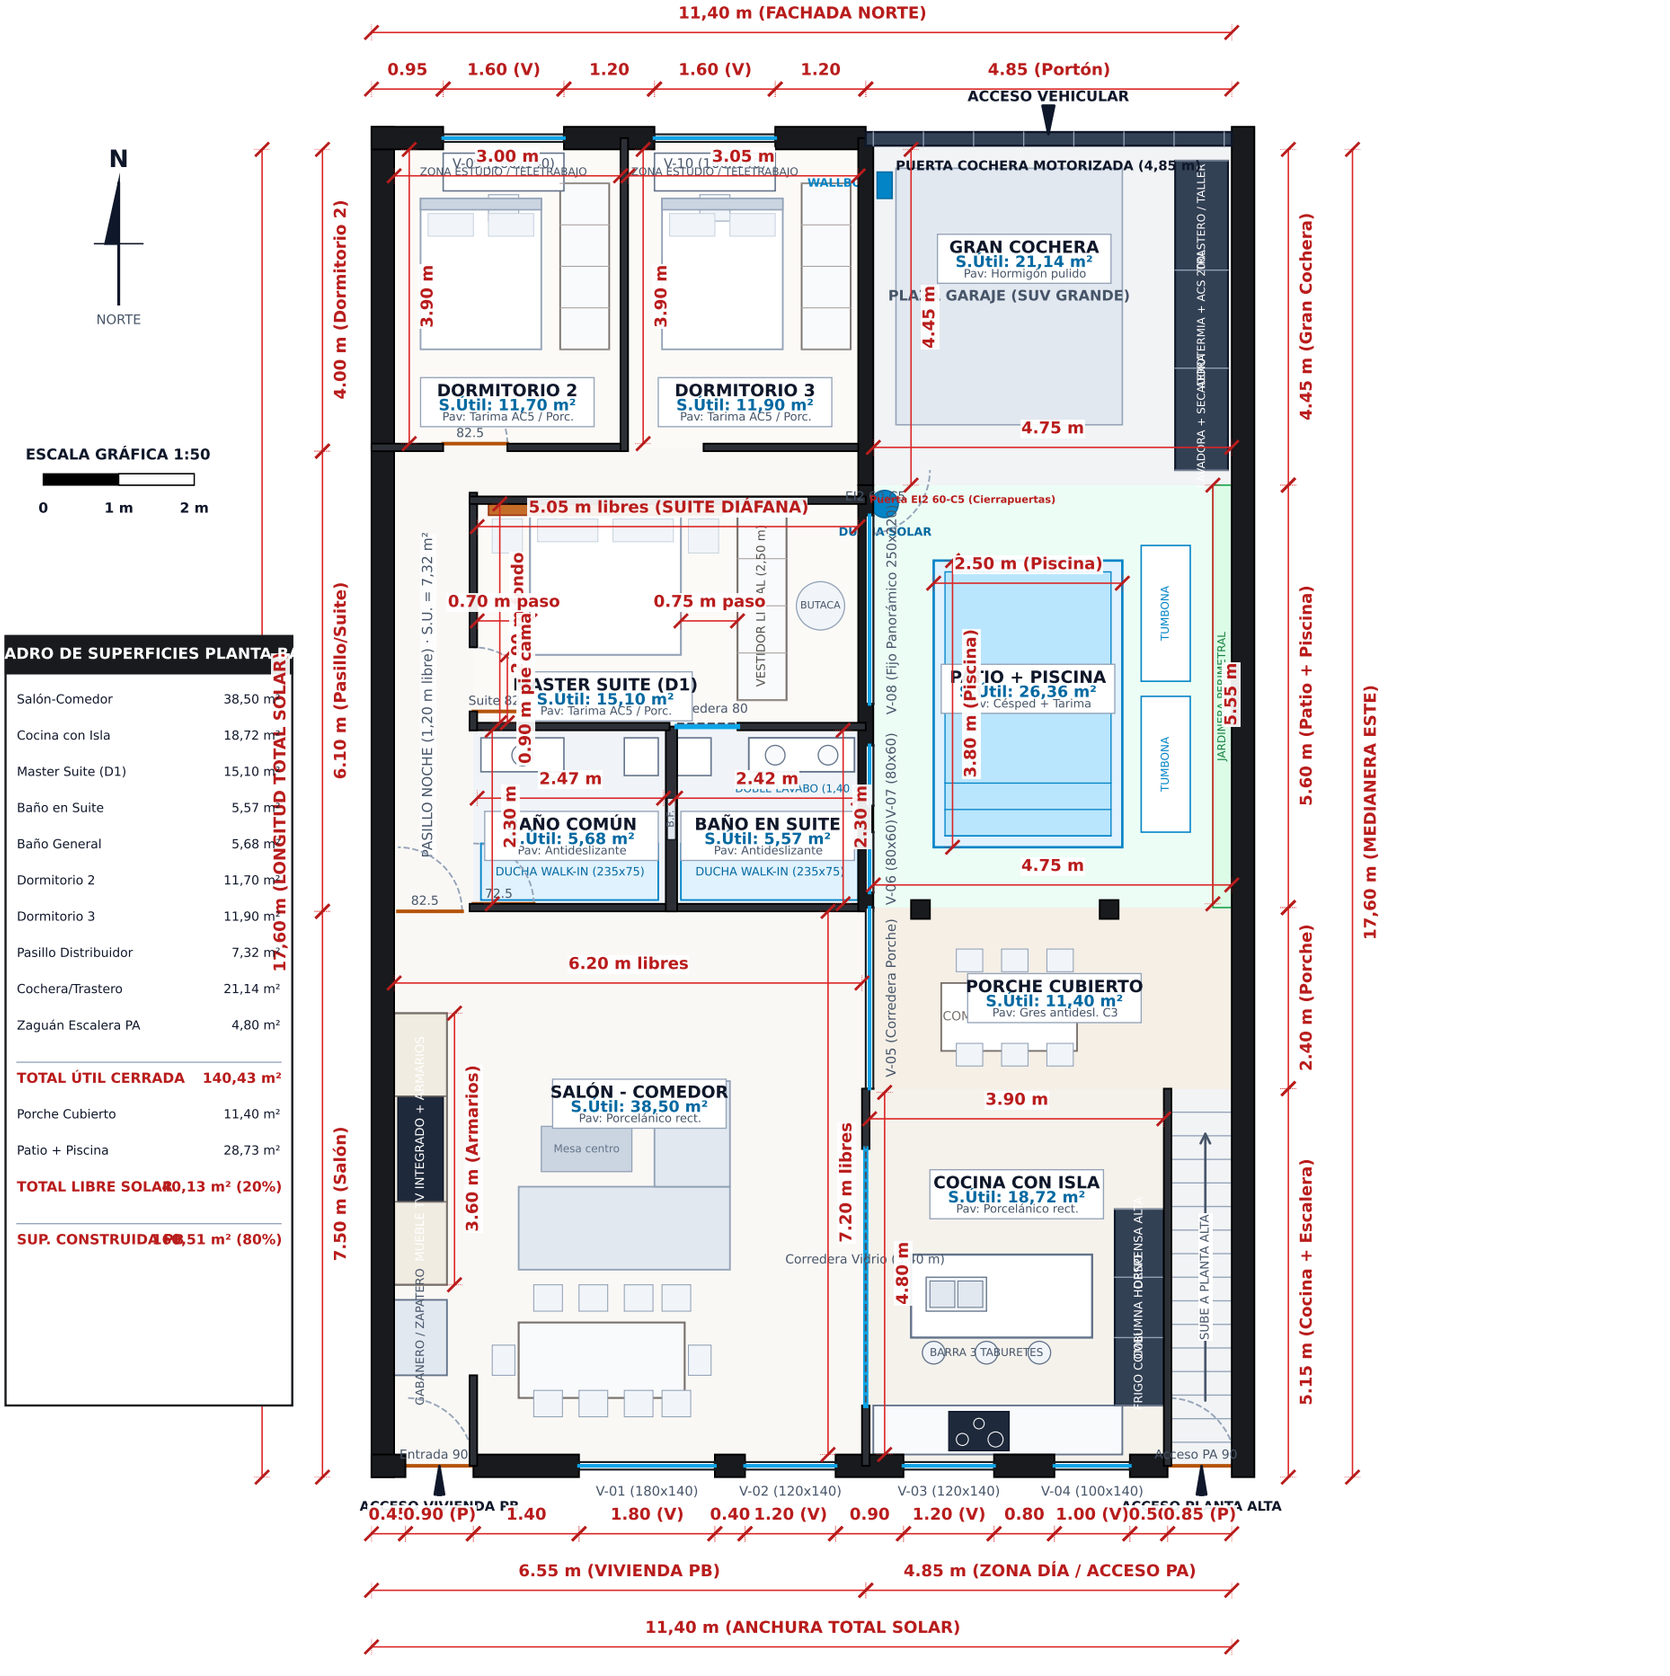

ADRO DE SUPERFICIES PLANTA B

Salón-Comedor	38,50 m²
Cocina con Isla	18,72 m²
Master Suite (D1)	15,10 m²
Baño en Suite	5,57 m²
Baño General	5,68 m²
Dormitorio 2	11,70 m²
Dormitorio 3	11,90 m²
Pasillo Distribuidor	7,32 m²
Cochera/Trastero	21,14 m²
Zaguán Escalera PA	4,80 m²
TOTAL ÚTIL CERRADA	**140,43 m²**
Porche Cubierto	11,40 m²
Patio + Piscina	28,73 m²
TOTAL LIBRE SOLAR	**40,13 m² (20%)**
SUP. CONSTRUIDA	**160,51 m² (80%)**

PROYECTO BÁSICO Y DE EJECUCIÓN

Vivienda Unifamiliar en PB + Espacio en Bruto en PA

Calle Moreno Torroba s/n · Palma del Río (Córdoba)

PLANO: P-01 PLANTA BAJA AMUEBLADA Y ACOTADA

Distribución Optimizada · Master Suite con Pasos Amplios + Garaje Trasero

S.Útil: 140,43 m² | Ocupación: 160,51 m² (80,0 % PGOU) | Patio: 40,13 m²


ESCALA: 1:50

FECHA: Octubre 2026

FORMATO: DIN A3

PLANO Nº

P-01

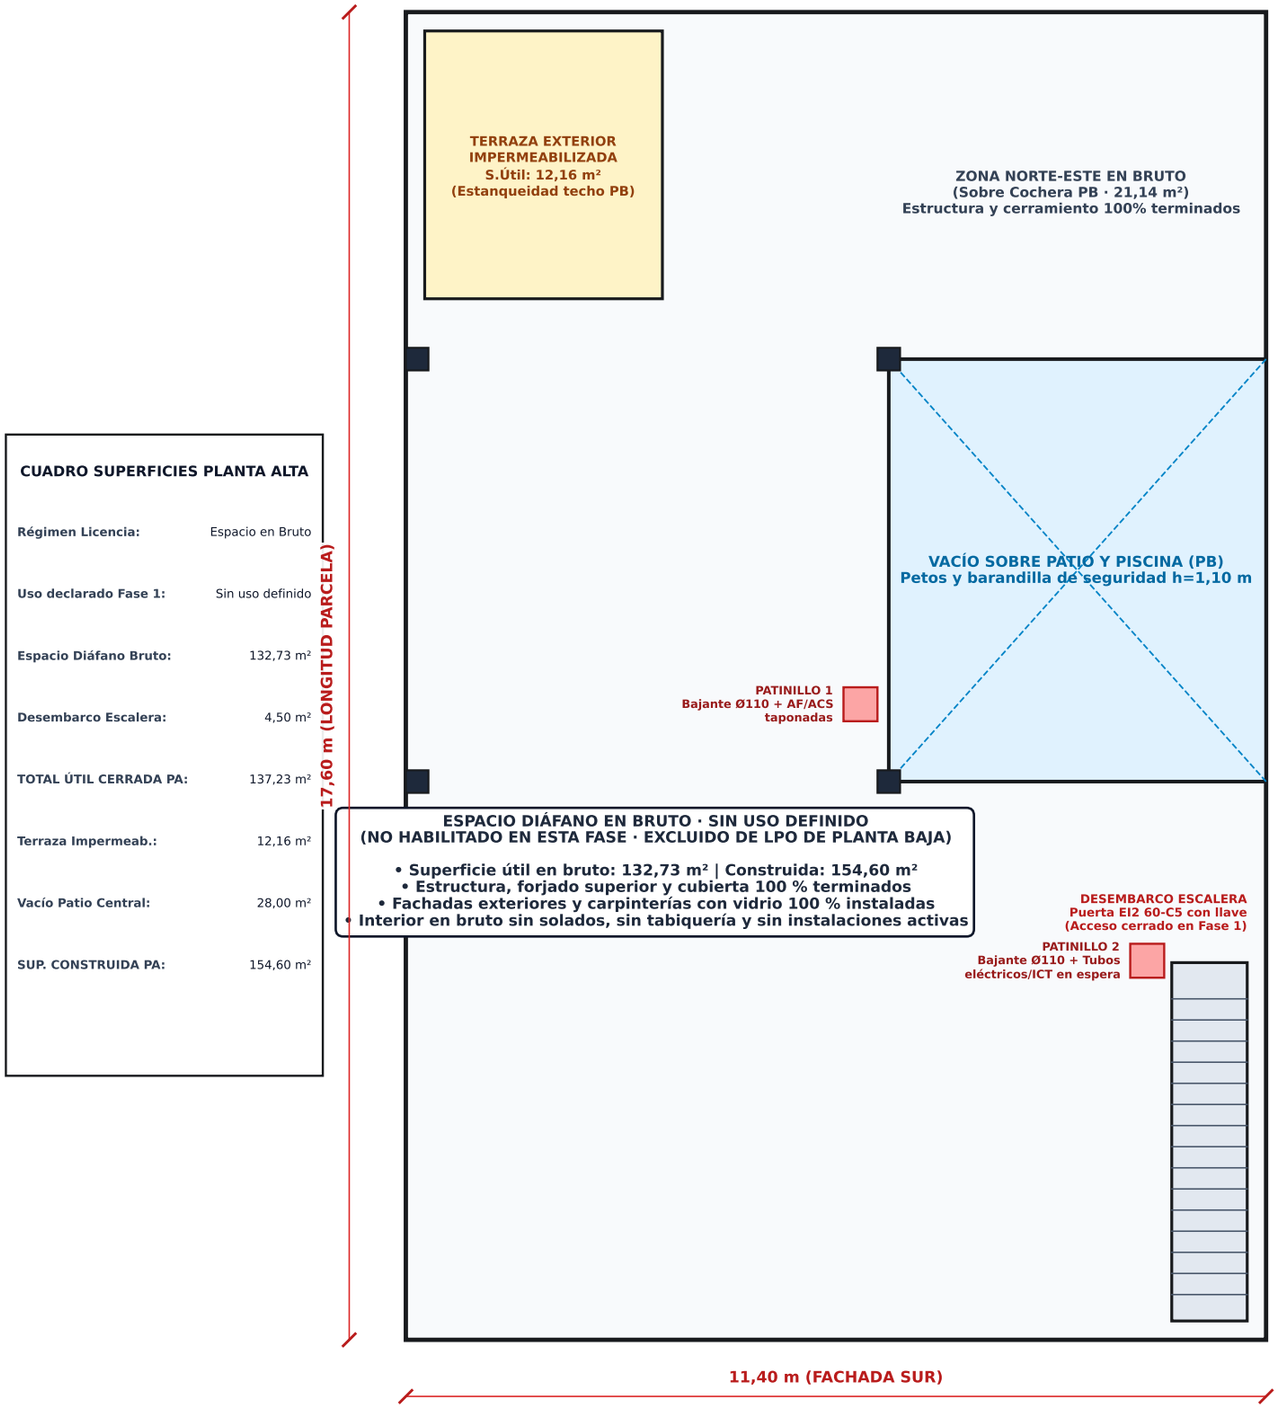

CUADRO SUPERFICIES PLANTA ALTA


Régimen Licencia:	Espacio en Bruto
Uso declarado Fase 1:	Sin uso definido
Espacio Diáfano Bruto:	132,73 m²
Desembarco Escalera:	4,50 m²
TOTAL ÚTIL CERRADA PA:	137,23 m²
Terraza Impermeab.:	12,16 m²
Vacío Patio Central:	28,00 m²
SUP. CONSTRUIDA PA:	154,60 m²

PROYECTO BÁSICO Y DE EJECUCIÓN
Vivienda Unifamiliar en PB + Espacio en Bruto en PA
Calle Moreno Torroba s/n · Palma del Río (Córdoba)

PLANO: PLANTA ALTA · ESPACIO DIÁFANO EN BRUTO (SIN USO)
Envolvente Exterior Terminada, Terraza Impermeabilizada y Acometidas en Espera
Documento Reglamentario CTE · Solicitud Licencia de Obras


ESCALA: 1:50
FECHA: Octubre 2026
FORMATO: DIN A3

PLANO Nº
P-02

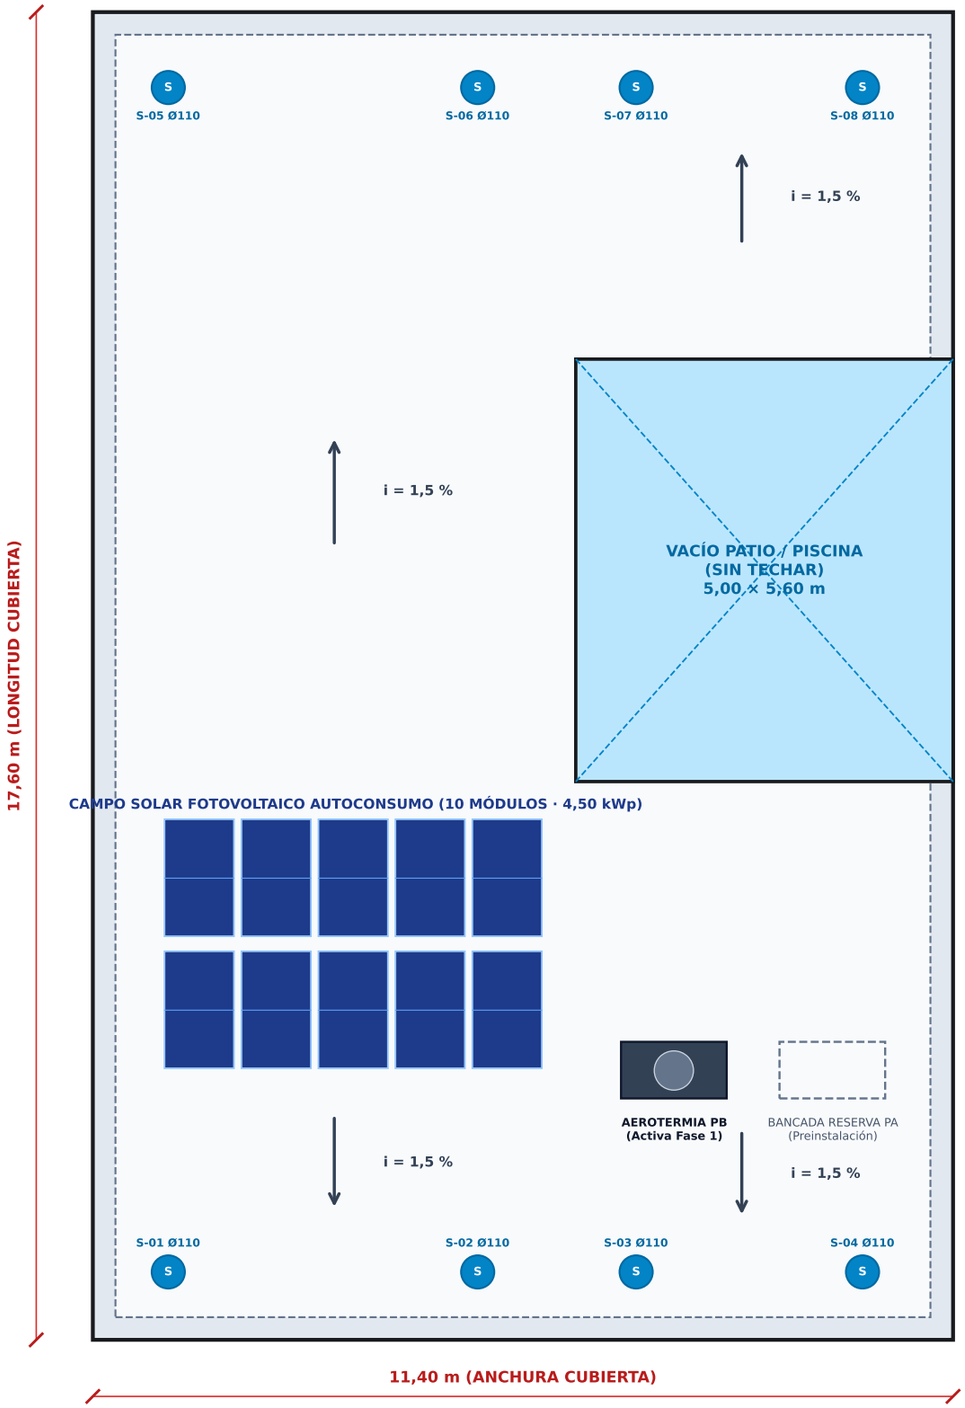


PROYECTO BÁSICO Y DE EJECUCIÓN Vivienda Unifamiliar en PB + Espacio en Bruto en PA **Calle Moreno Torroba s/n · Palma del Río (Córdoba)**	**PLANO: PLANTA DE CUBIERTAS E INSTALACIONES** Cubierta Plana Invertida (XPS 100 mm), Sumideros Sifónicos, Aerotermia y Fotovoltaica **Documento Reglamentario CTE · Solicitud Licencia de Obras**	**ESCALA: 1:100** FECHA: Octubre 2026 FORMATO: DIN A3	PLANO Nº **P-03**

ALZADO PRINCIPAL SUR (CALLE MORENO TORROBA)

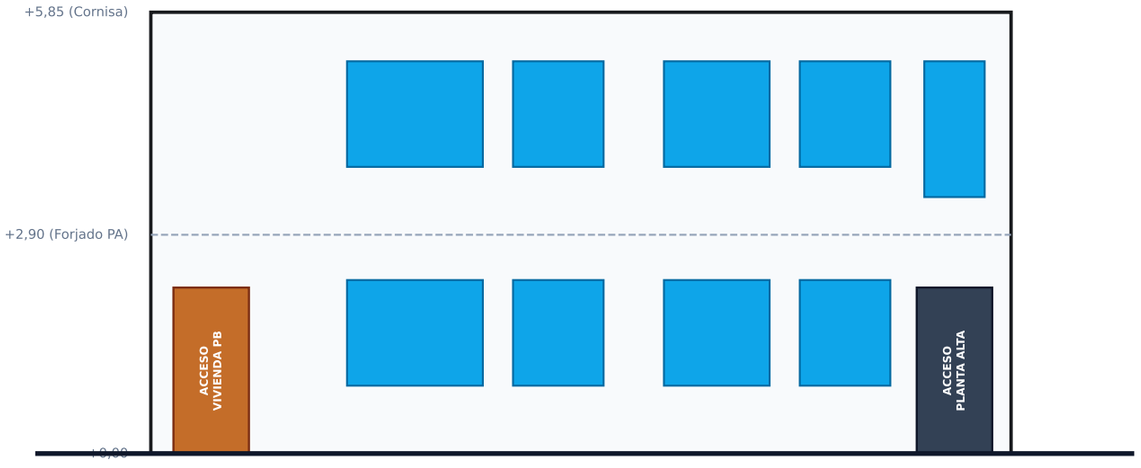


ALZADO TRASERO NORTE (VIAL ACCESO RODADO COCHERA)

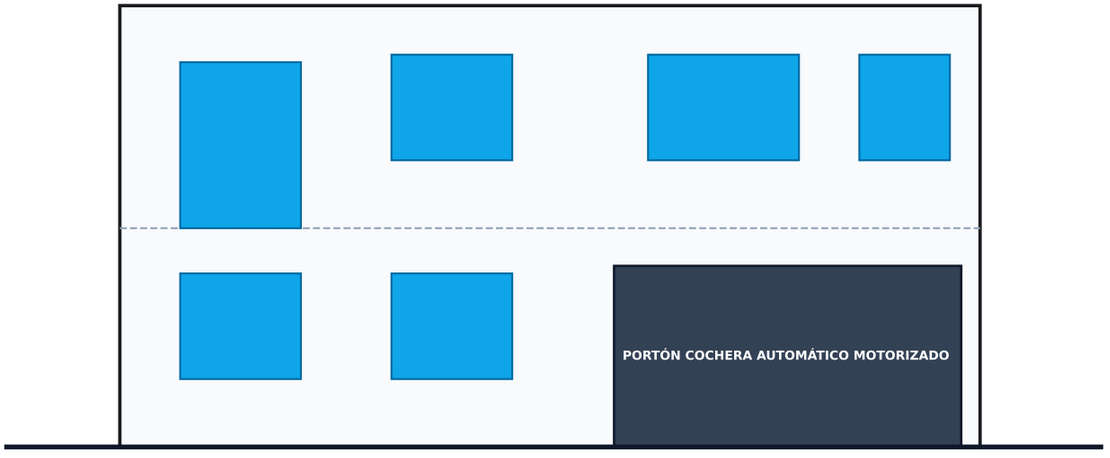

PROYECTO BÁSICO Y DE EJECUCIÓN Vivienda Unifamiliar en PB + Espacio en Bruto en PA **Calle Moreno Torroba s/n · Palma del Río (Córdoba)**	**PLANO: ALZADOS EXTERIORES GENERALES** Alzado Principal Sur (Moreno Torroba) y Alzado Trasero Norte (Garaje) **Documento Reglamentario CTE · Solicitud Licencia de Obras**	**ESCALA: 1:100** FECHA: Octubre 2026 FORMATO: DIN A3	**PLANO Nº** **P-04**


SECCIÓN LONGITUDINAL CONSTRUCTIVA A-A'

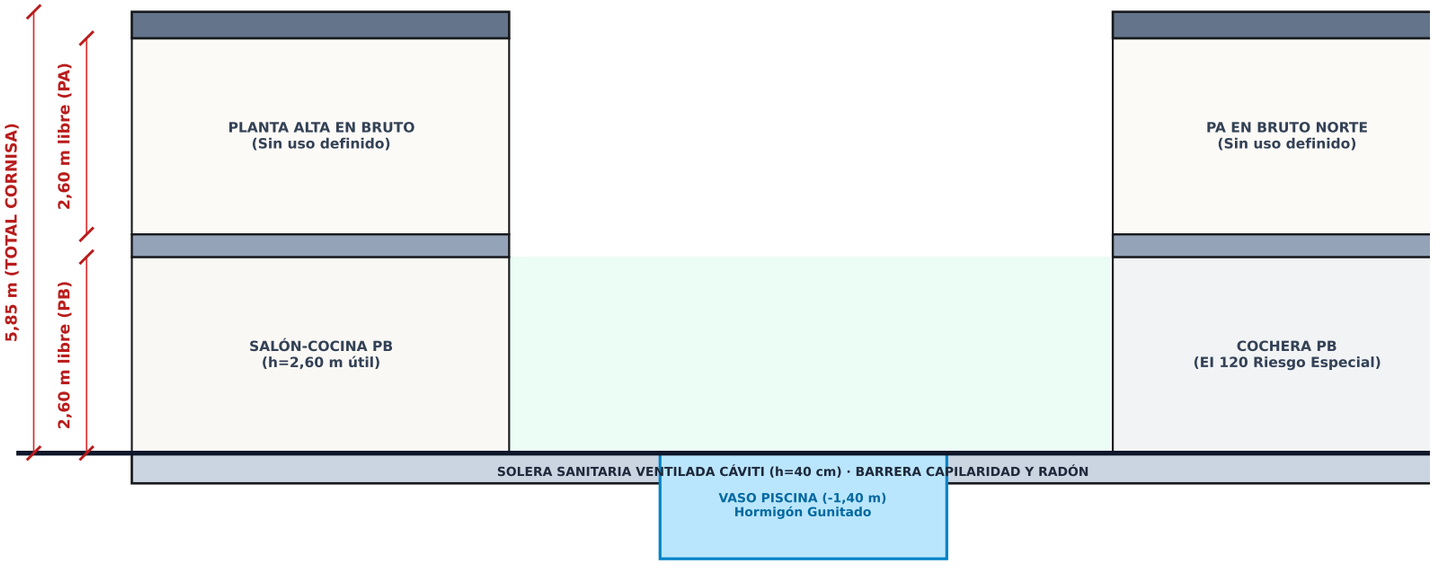

SECCIÓN TRANSVERSAL CONSTRUCTIVA B-B' (CRUJÍA CENTRAL Y CIMENTACIÓN)




PROYECTO BÁSICO Y DE EJECUCIÓN Vivienda Unifamiliar en PB + Espacio en Bruto en PA **Calle Moreno Torroba s/n · Palma del Río (Córdoba)**	**PLANO: SECCIONES CONSTRUCTIVAS GENERALES** Sección Longitudinal A-A' y Sección Transversal B-B' con Cimentación (-1,50 m) y Alturas **Documento Reglamentario CTE · Solicitud Licencia de Obras**	**ESCALA: 1:75** FECHA: Octubre 2026 FORMATO: DIN A3	PLANO Nº **P-05**

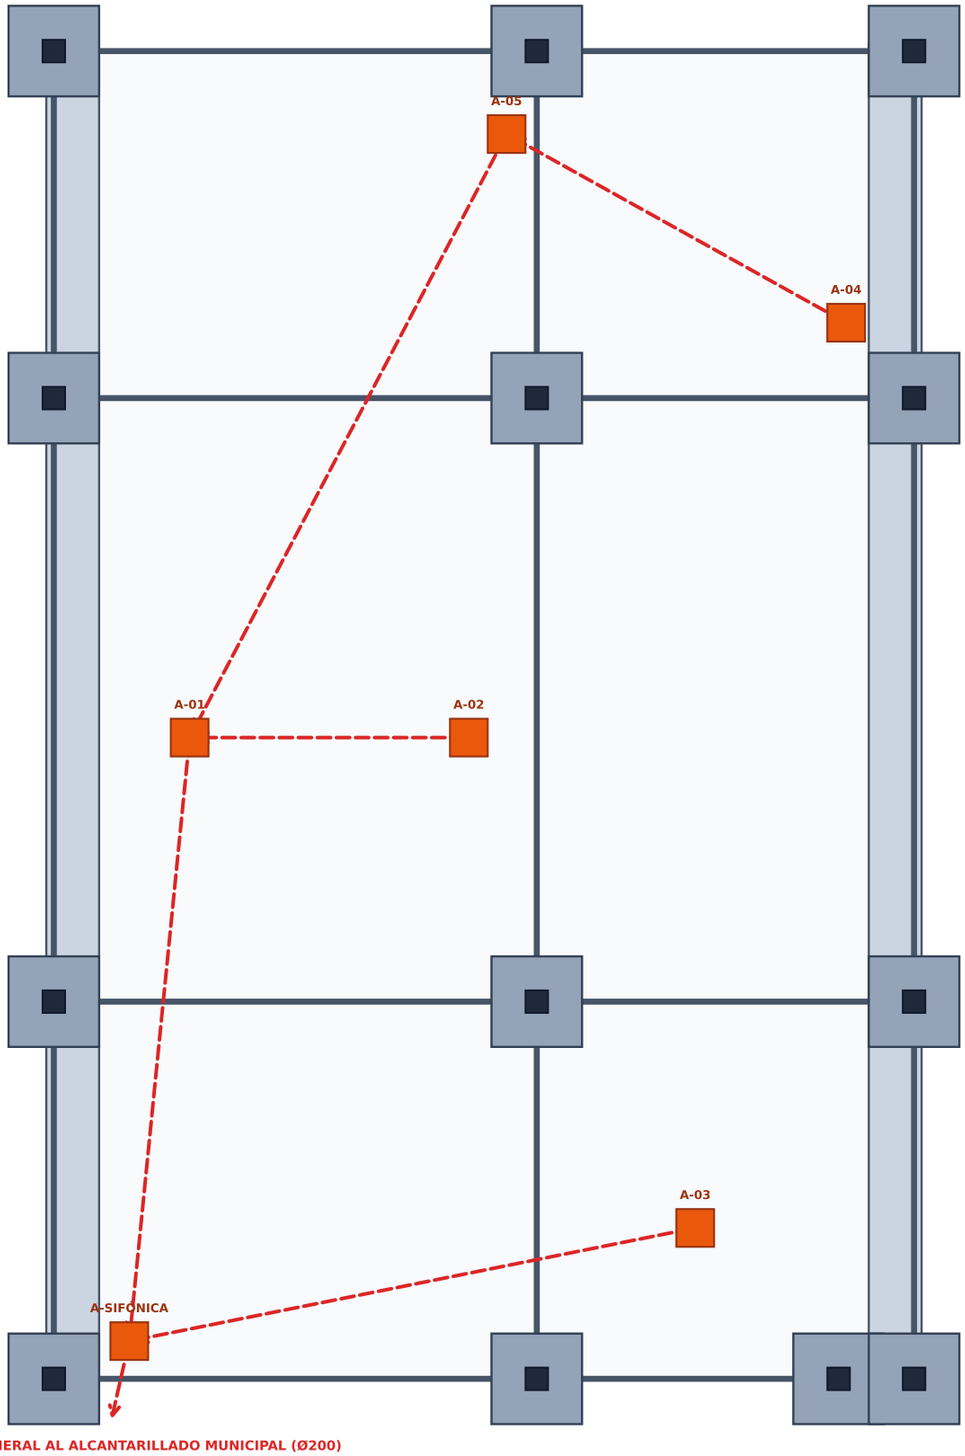

CUADRO DE CONTROL DE ESTRUCTURA

- Normativa: Código Estructural (RD 470/2021)
- Hormigón Zapatas: HA-25/B/20/IIa
- Hormigón Vigas/Pilares: HA-25/B/20/IIa
- Acero Armaduras: B 500 S (soldable)
- Recubrimiento mínimo: 40 mm en zapatas
- Cota de cimentación: -1,50 m
- Tensión admisible terreno: 1,80 kg/cm²
- Solera Sanitaria: Tipo Cáviti h=40 cm
- Saneamiento: PVC SN4 Ø160 mm al 2,0%

PROYECTO BÁSICO Y DE EJECUCIÓN Vivienda Unifamiliar en PB + Espacio en Bruto en PA **Calle Moreno Torroba s/n · Palma del Río (Córdoba)**	**PLANO: ESTRUCTURA Y CIMENTACIÓN** Plano de Replanteo de Zapatas, Vigas Riostras y Red de Saneamiento Enterrada **Documento Reglamentario CTE · Solicitud Licencia de Obras**	**ESCALA: 1:75** FECHA: Octubre 2026 FORMATO: DIN A3	PLANO Nº **P-06**

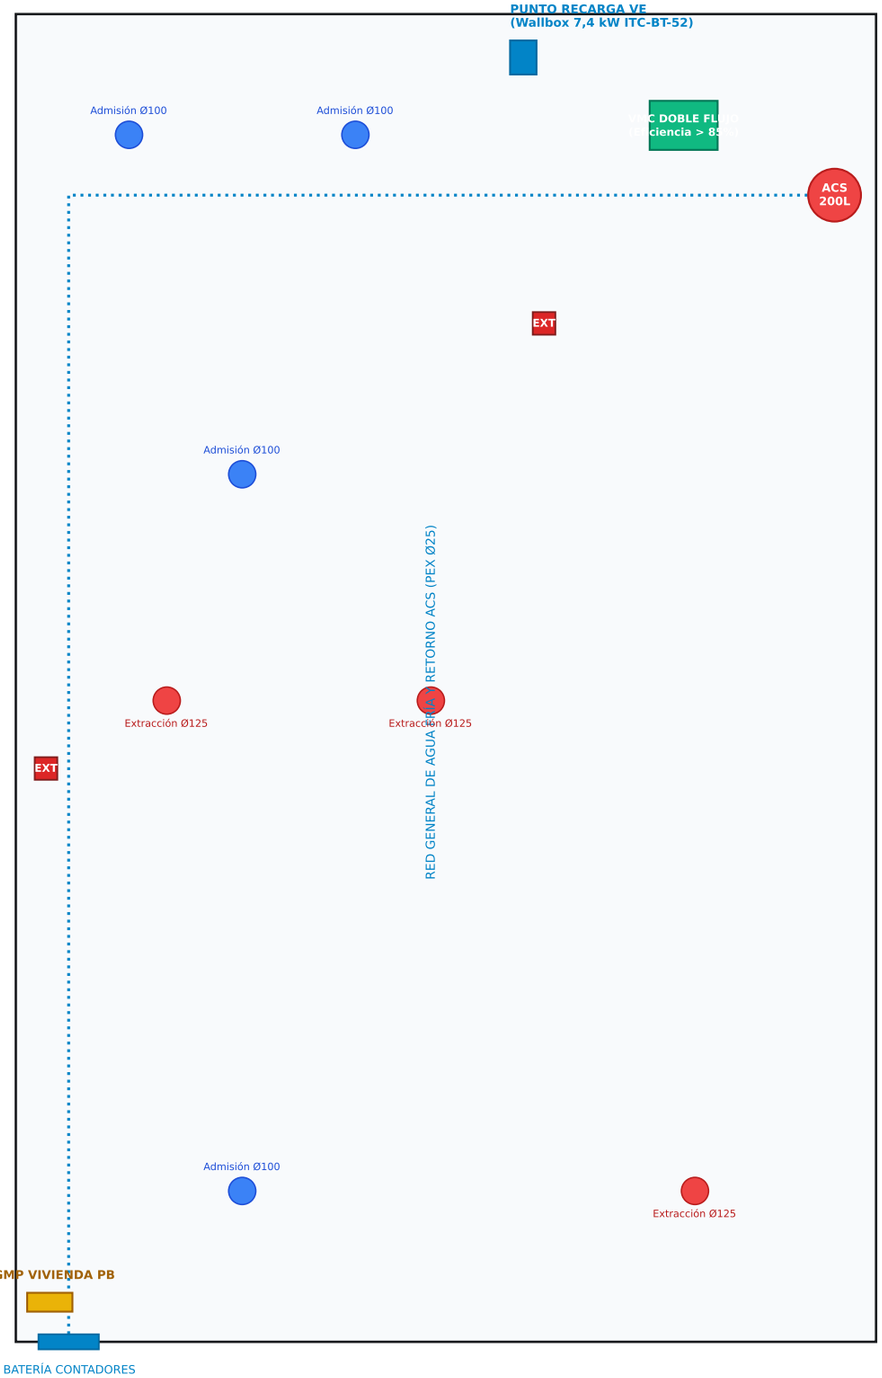

SIMBOLOGÍA DE INSTALACIONES (CTE)

[CGMP]

Cuadro Eléctrico General con IGA, ID y PIAs

[Wallbox]

Recarga VE Tipo 2 Modo 3 (7,4 kW) REBT ITC-BT-52

[Aerotermia]

Bomba de Calor Inverter Clase A+++ (COP > 4.2)

[ACS 200L]

Interacumulador Vitrificado con Apoyo Solar

[VMC]

Ventilación Mecánica Doble Flujo DB-HS3

[Admisión]

Boca de impulsión de aire filtrado en estancias secas

[Extracción]

Boca de extracción de aire viciado en húmedas

[EXT 21A]

Extintor de polvo polivalente ABC 6 kg (DB-SI)

PROYECTO BÁSICO Y DE EJECUCIÓN Vivienda Unifamiliar en PB + Espacio en Bruto en PA **Calle Moreno Torroba s/n · Palma del Río (Córdoba)**	**PLANO: INSTALACIONES GENERALES** Climatización Aerotérmica, Suelo Radiante, VMC, Electricidad, Wallbox y Fontanería **Documento Reglamentario CTE · Solicitud Licencia de Obras**	**ESCALA: 1:75** FECHA: Octubre 2026 FORMATO: DIN A3	**PLANO Nº** **P-07**