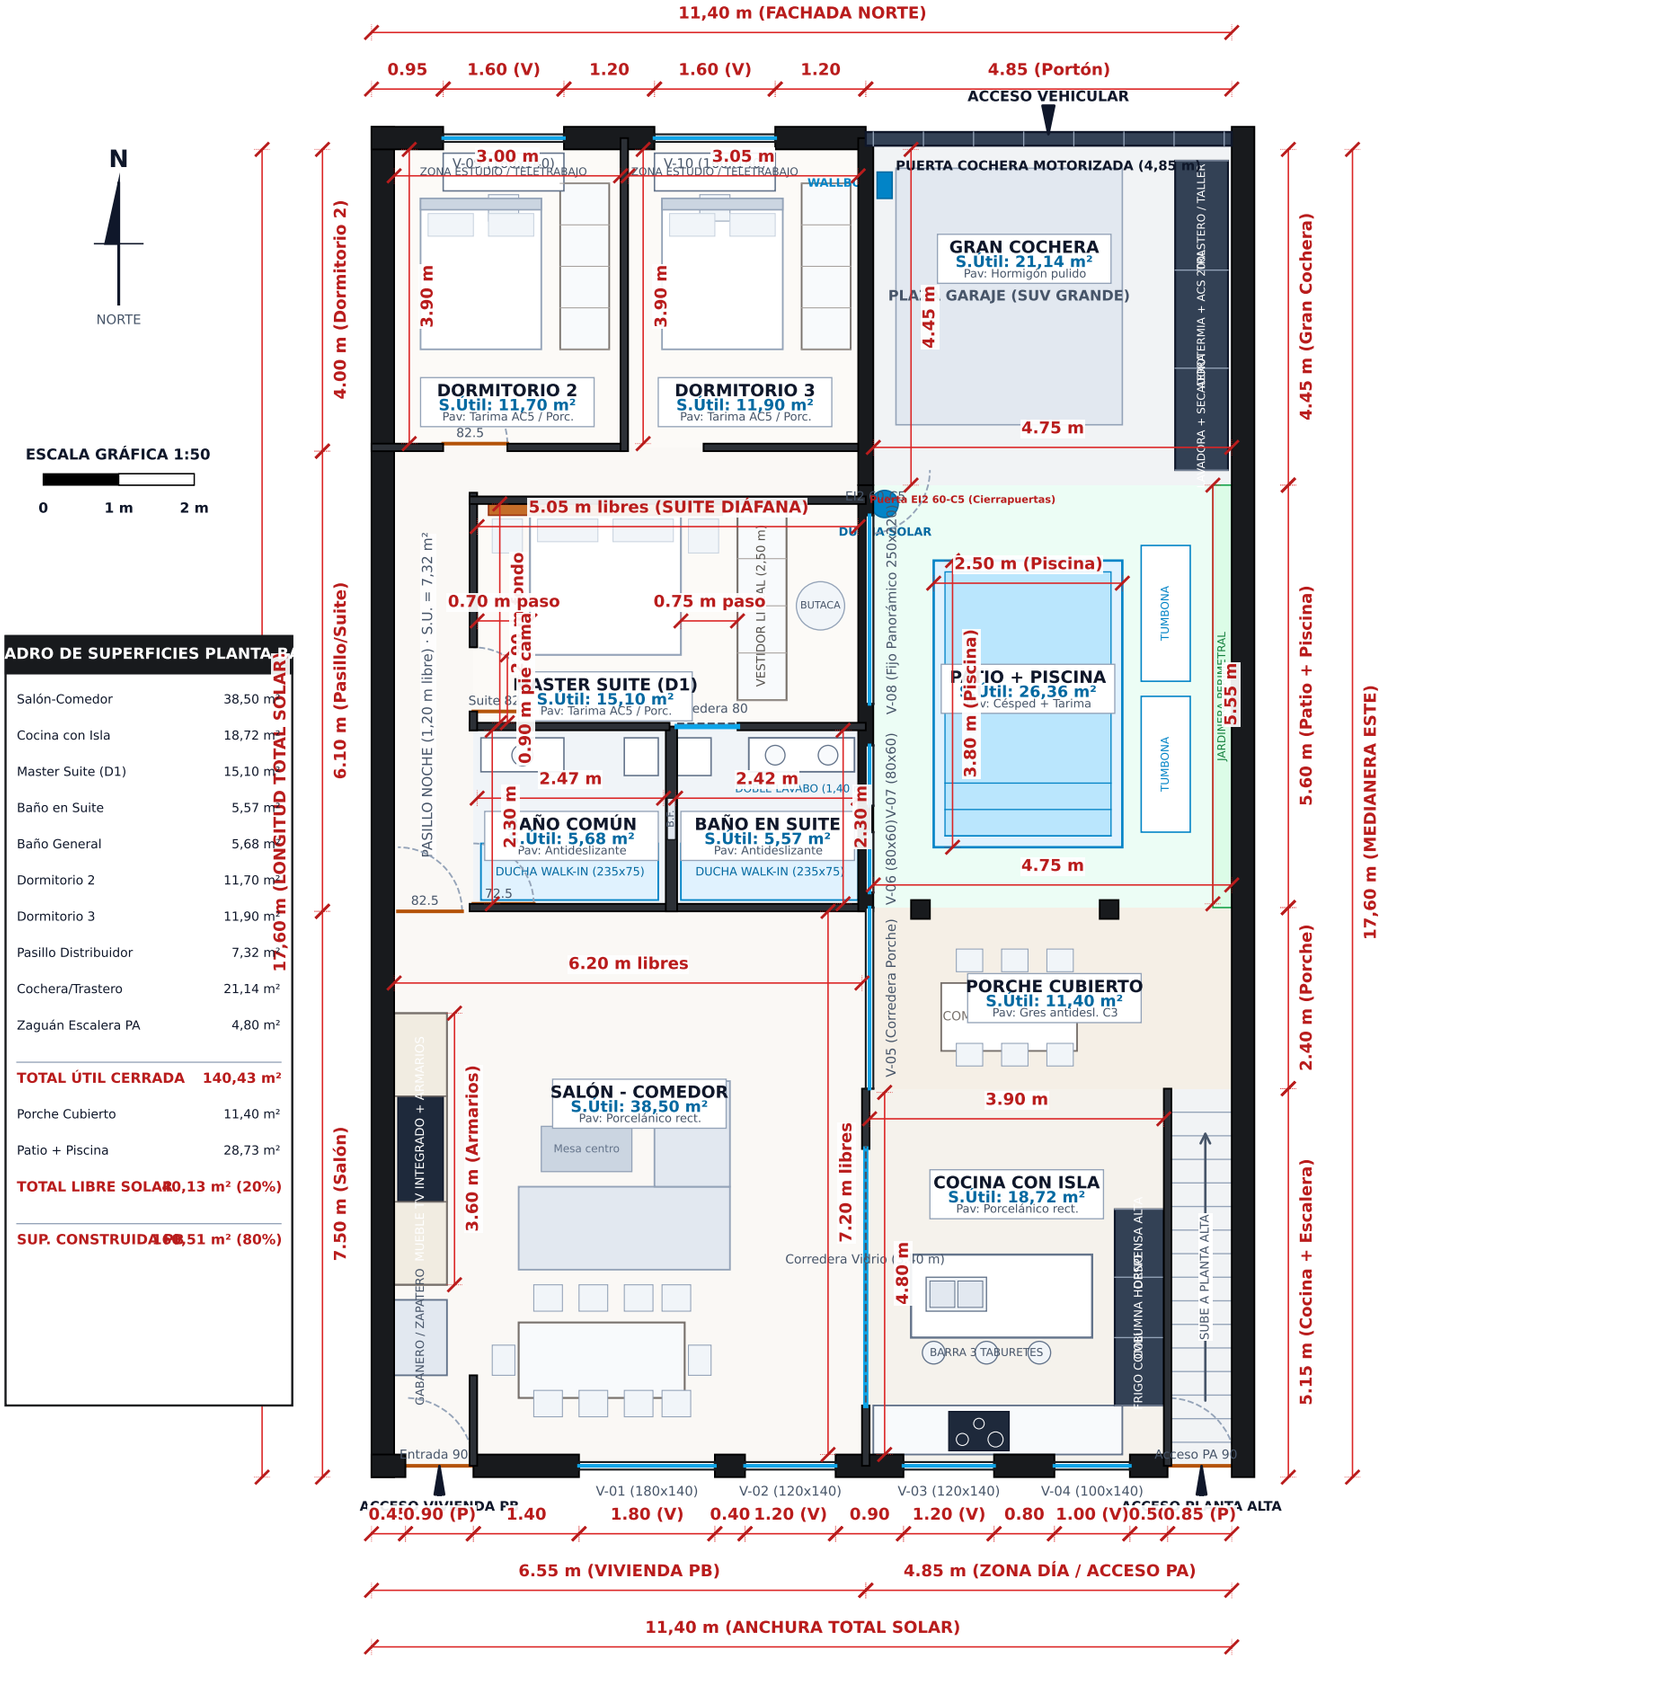


ADRO DE SUPERFICIES PLANTA B

Salón-Comedor	38,50 m²
Cocina con Isla	18,72 m²
Master Suite (D1)	15,10 m²
Baño en Suite	5,57 m²
Baño General	5,68 m²
Dormitorio 2	11,70 m²
Dormitorio 3	11,90 m²
Pasillo Distribuidor	7,32 m²
Cochera/Trastero	21,14 m²
Zaguán Escalera PA	4,80 m²
TOTAL ÚTIL CERRADA	**140,43 m²**
Porche Cubierto	11,40 m²
Patio + Piscina	28,73 m²
TOTAL LIBRE SOLAR	**40,13 m² (20%)**
SUP. CONSTRUIDA	**160,51 m² (80%)**

PROYECTO BÁSICO Y DE EJECUCIÓN

Vivienda Unifamiliar en PB + Espacio en Bruto en PA

Calle Moreno Torroba s/n · Palma del Río (Córdoba)

PLANO: P-01 PLANTA BAJA AMUEBLADA Y ACOTADA

Distribución Optimizada · Master Suite con Pasos Amplios + Garaje Trasero

S.Útil: 140,43 m² | Ocupación: 160,51 m² (80,0 % PGOU) | Patio: 40,13 m²

ESCALA: 1:50

FECHA: Octubre 2026

FORMATO: DIN A3

PLANO Nº

P-01