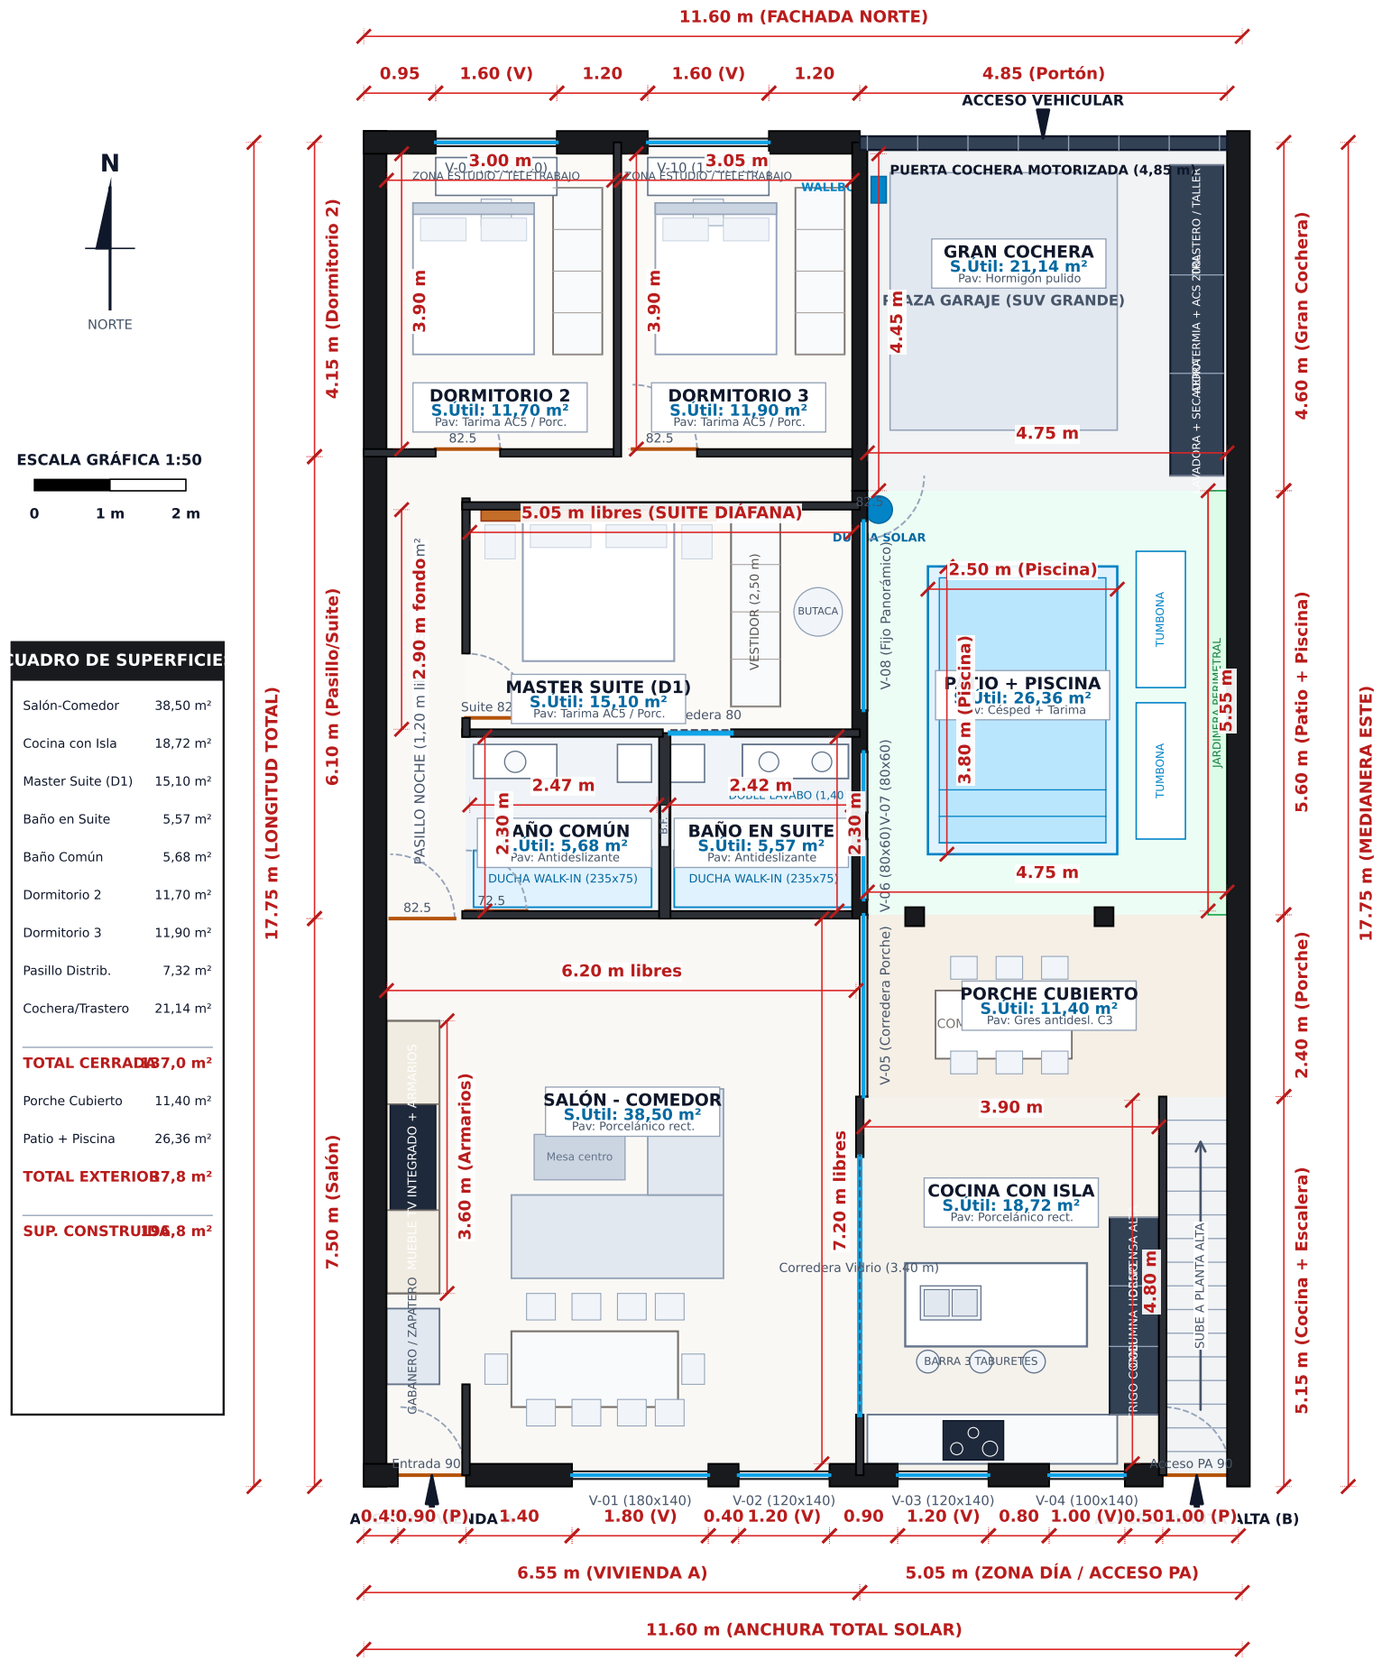


CUADRO DE SUPERFICIES

Salón-Comedor	38,50 m²
Cocina con Isla	18,72 m²
Master Suite (D1)	15,10 m²
Baño en Suite	5,57 m²
Baño Común	5,68 m²
Dormitorio 2	11,70 m²
Dormitorio 3	11,90 m²
Pasillo Distrib.	7,32 m²
Cochera/Trastero	21,14 m²
TOTAL CERRADA	**137,0 m²**
Porche Cubierto	11,40 m²
Patio + Piscina	26,36 m²
TOTAL EXTERIOR	**37,8 m²**
SUP. CONSTRUIDA	**196,8 m²**

PROYECTO RESIDENCIAL BIFAMILIAR — **PLANO: PLANTA BAJA AMUEBLADA Y ACOTADA** — **ESCALA: 1:50 (A3)**

Vivienda Unifamiliar en Parcela Pasante con Patio y Piscina Distribución Optimizada · Master Suite con Pasos Amplios + Vestidor 2,50 m — FECHA: Agosto 2026

Calle Moreno Torroba s/n · Palma del Río (Córdoba) — **Superficie Útil Cerrada: 137,00 m² | Exterior: 37,80 m² | Constr.: 196,80 m²** — FORMATO: DIN A3

PLANO Nº **P-01**



SUPERFICIES PLANTA ALTA	
Salón-Comedor	48,20 m²
Cocina con Isla	18,72 m²
Master Suite (D1)	15,10 m²
Baño en Suite	5,57 m²
Baño Común	5,68 m²
Dormitorio 2 (Ext)	21,14 m²
Dormitorio 3	11,00 m²
Pasillo Distrib.	7,32 m²
Desembarco Esc.	4,50 m²
TOTAL CERRADO	**137,23 m²**
Terraza Solárium	12,16 m²
Vacío Patio (PB)	28,00 m²
TOTAL EXTERIOR	**12,16 m²**
SUP. CONSTRUIDA	**154,60 m²**

PROYECTO RESIDENCIAL BIFAMILIAR — PLANO: PLANTA ALTA (VIVIENDA B) AMUEBLADA Y ACOTADA — ESCALA 1:50 (A3)


Vivienda Unifamiliar en Parcela Pasante con Patio y Piscina Distribución Ejecutiva · 3 Dormitorios, 2 Baños, Gran Salón y Terraza Solárium

Calle Moreno Torroba s/n · Palma del Río (Córdoba) — **Superficie Útil Cerrada: 137,23 m² | Exterior: 12,16 m² | Constr.: 154,60 m²**

FECHA: Octubre 2026

FORMATO: DIN A3

PLANO Nº **P-02**

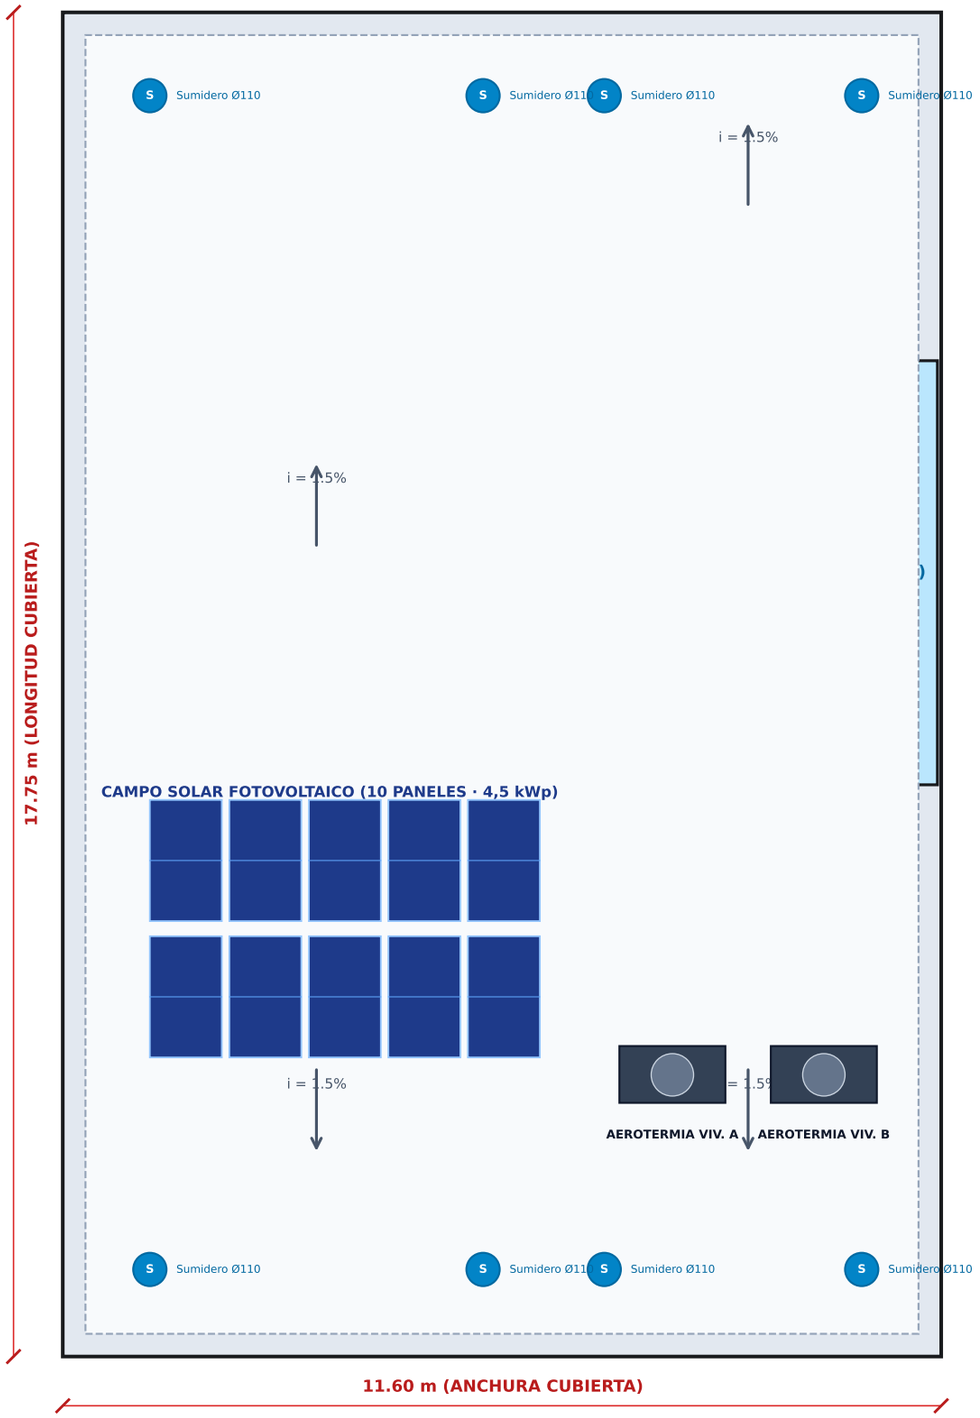

PROYECTO RESIDENCIAL BIFAMILIAR | **PLANO: PLANTA DE CUBIERTAS E INSTALACIONES** | **ESCALA: 1:100 (A3)**

Vivienda Unifamiliar en Parcela Pasante con Patio y Piscina Cubierta Plana Invertida, Campo Solar Fotovoltaico y Climatización

Calle Moreno Torroba s/n · Palma del Río (Córdoba) | **Documento de Ejecución CTE · Aprobación de Licencia Municipal**


FECHA: Octubre 2026

FORMATO: DIN A3


PLANO Nº

P-03

ALZADO PRINCIPAL SUR (CALLE MORENO TORROBA)

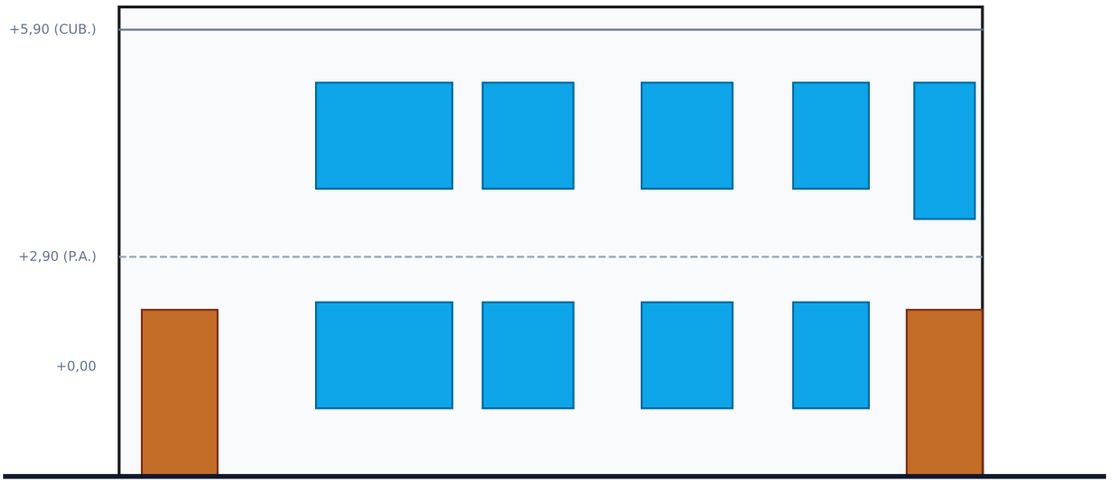

ALZADO TRASERO NORTE (CALLE POSTERIOR · GARAJE)

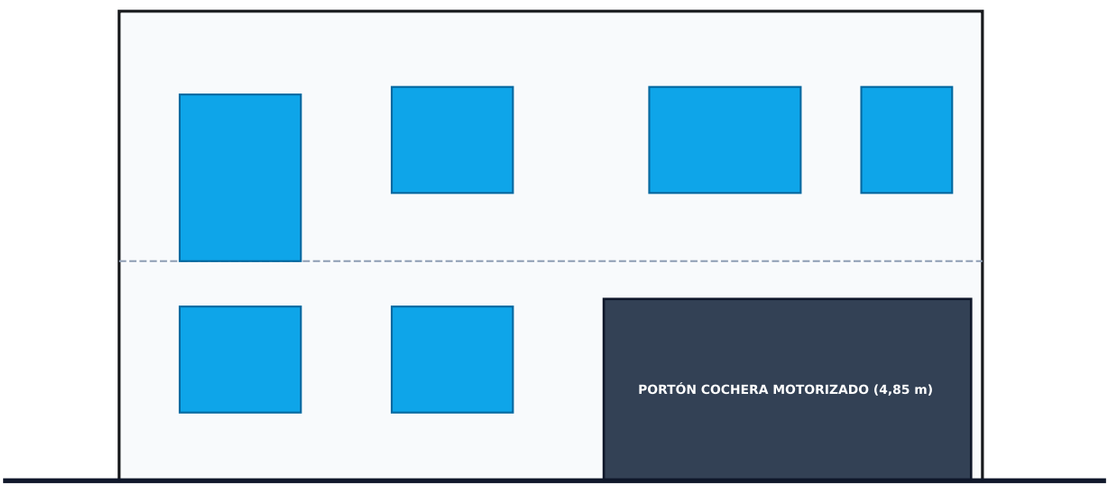


PROYECTO RESIDENCIAL BIFAMILIAR
Vivienda Unifamiliar en Parcela Pasante con Patio y Piscina
Calle Moreno Torroba s/n · Palma del Río (Córdoba)

PLANO: ALZADOS EXTERIORES GENERALES
Alzado Principal Sur (Moreno Torroba) y Alzado Trasero Norte (Garaje)
Documento de Ejecución CTE · Aprobación de Licencia Municipal

ESCALA: 1:100 (A3)
FECHA: Octubre 2026
FORMATO: DIN A3

PLANO Nº
P-04

SECCIÓN LONGITUDINAL CONSTRUCTIVA A-A'

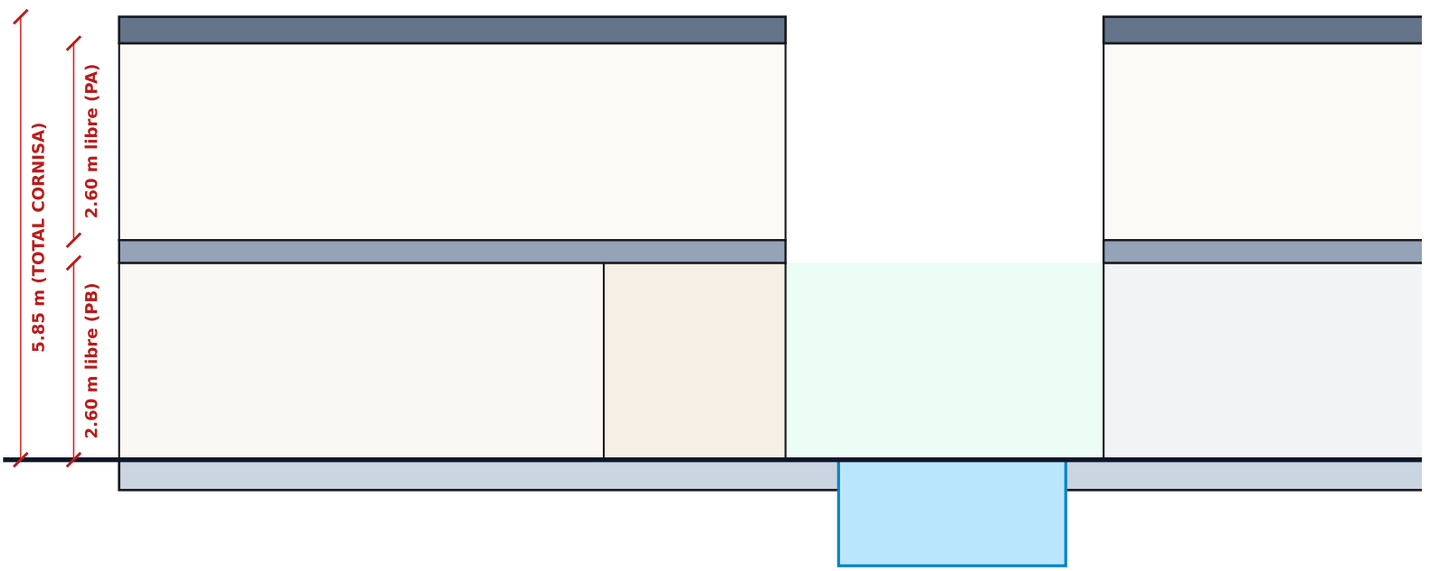

SECCIÓN TRANSVERSAL CONSTRUCTIVA B-B' (CRUJÍA CENTRAL Y CIMENTACIÓN)




PROYECTO RESIDENCIAL BIFAMILIAR | **PLANO: SECCIONES CONSTRUCTIVAS GENERALES** | **ESCALA: 1:75 (A3)**

Vivienda Unifamiliar en Parcela Pasante con Patio y Piscina Sección Longitudinal A-A' y Sección Transversal B-B' con Cimentación y Alturas | FECHA: Octubre 2026

Calle Moreno Torroba s/n · Palma del Río (Córdoba) | **Documento de Ejecución CTE · Aprobación de Licencia Municipal** | FORMATO: DIN A3

PLANO Nº
P-05

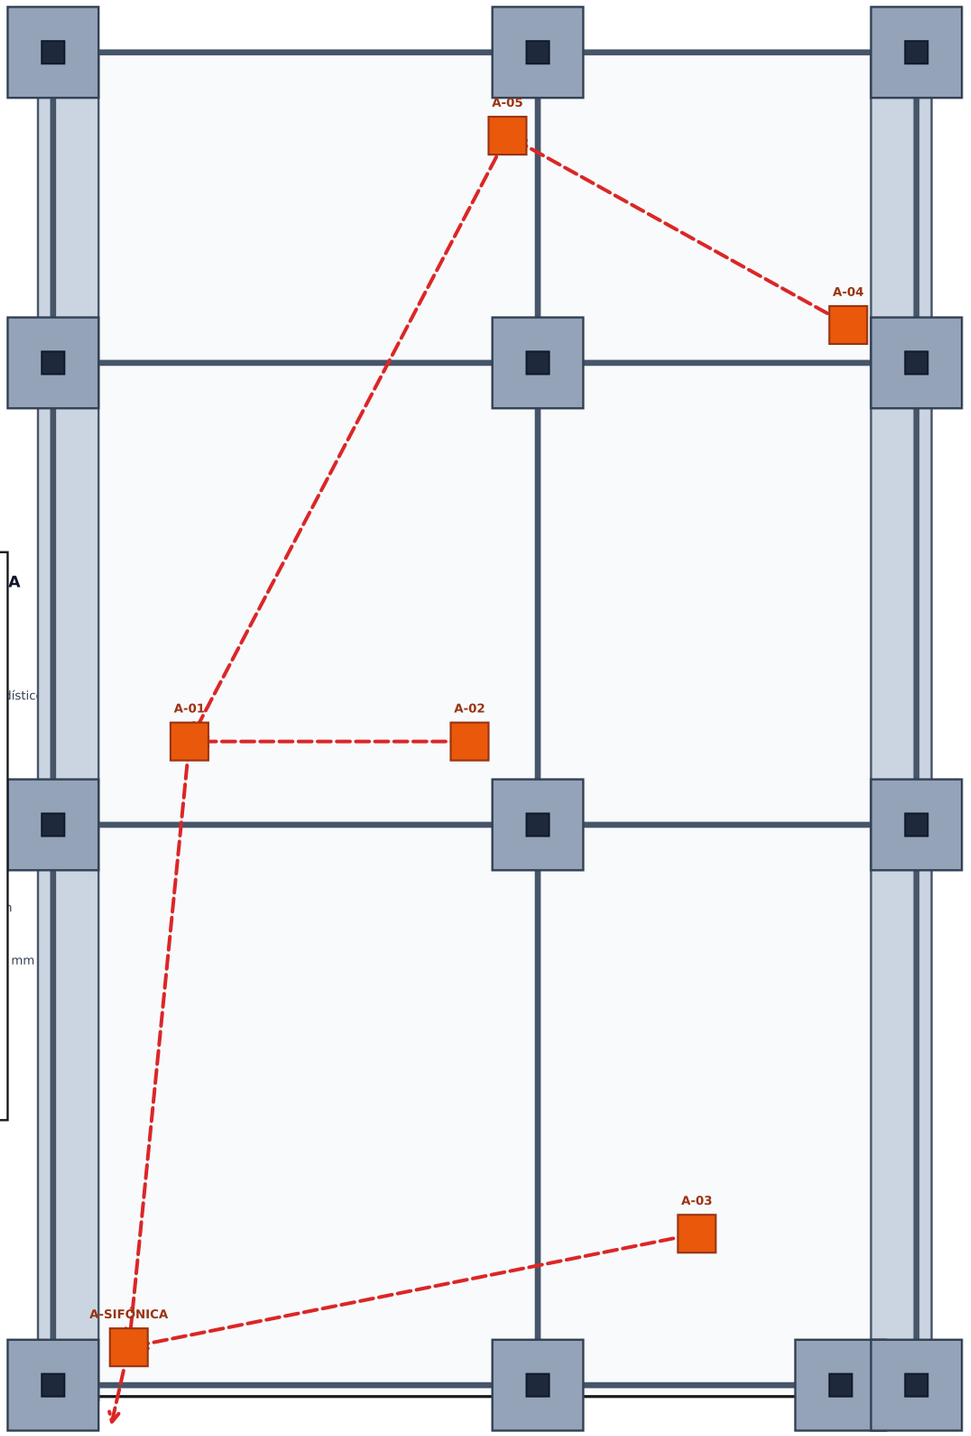

C A

lístic

n


mm

PROYECTO RESIDENCIAL BIFAMILIAR
Vivienda Unifamiliar en Parcela Pasante con Patio y Piscina
Calle Moreno Torroba s/n · Palma del Río (Córdoba)

PLANO: ESTRUCTURA Y CIMENTACIÓN
Plano de Replanteo de Zapatas, Vigas Riostras y Red de Saneamiento Enterrada
Documento de Ejecución CTE · Aprobación de Licencia Municipal

ESCALA: 1:75 (A3)
FECHA: Octubre 2026
FORMATO: DIN A3

PLANO Nº
P-06

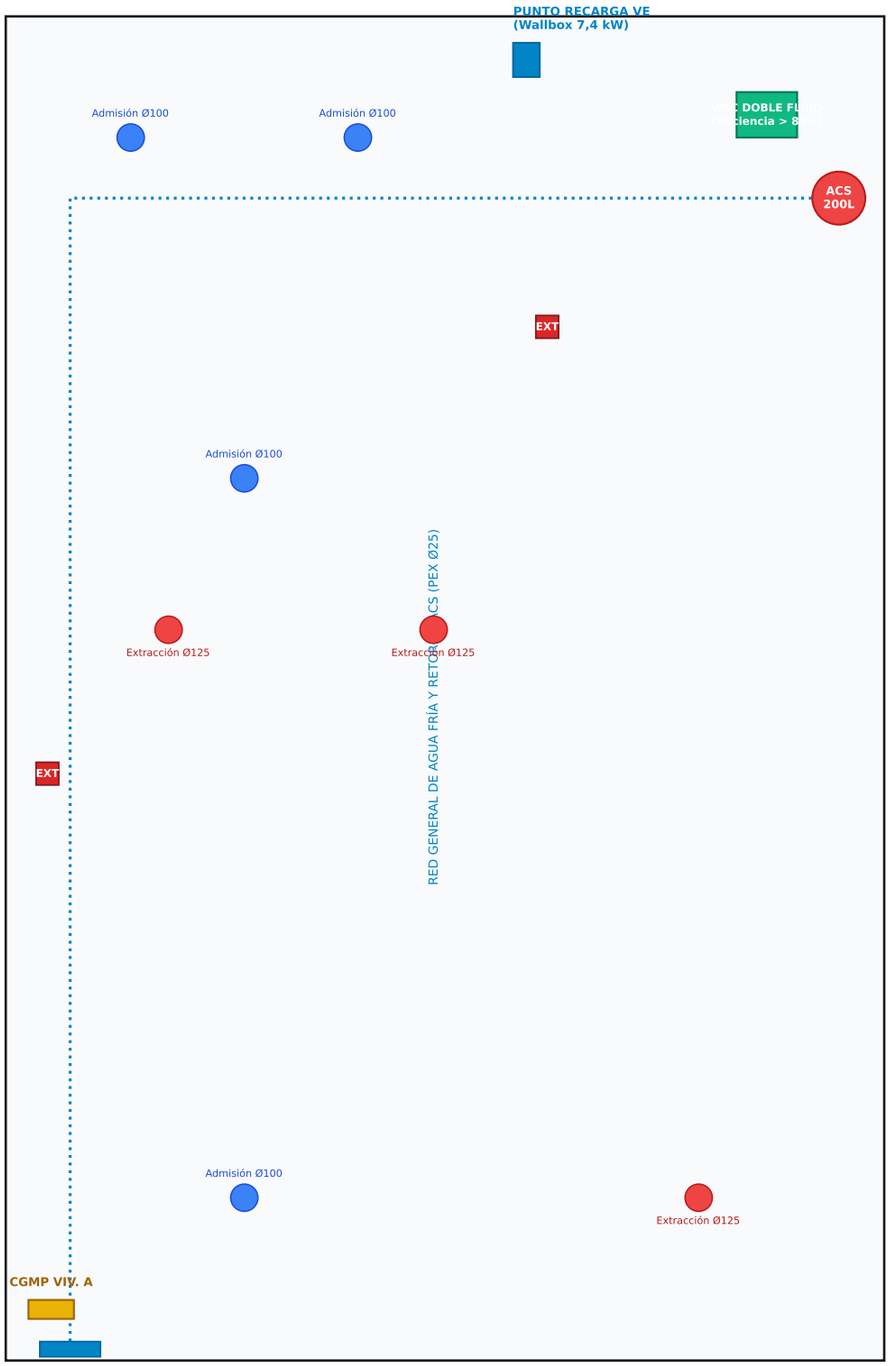

PROYECTO RESIDENCIAL BIFAMILIAR
Vivienda Unifamiliar en Parcela Pasante con Patio y Piscina
Calle Moreno Torroba s/n · Palma del Río (Córdoba)

PLANO: INSTALACIONES GENERALES
Climatización Aerotérmica, Suelo Radiante, VMC, Electricidad, Wallbox y Fontanería
Documento de Ejecución CTE · Aprobación de Licencia Municipal

ESCALA: 1:75 (A3)
FECHA: Octubre 2026
FORMATO: DIN A3

PLANO Nº
P-07