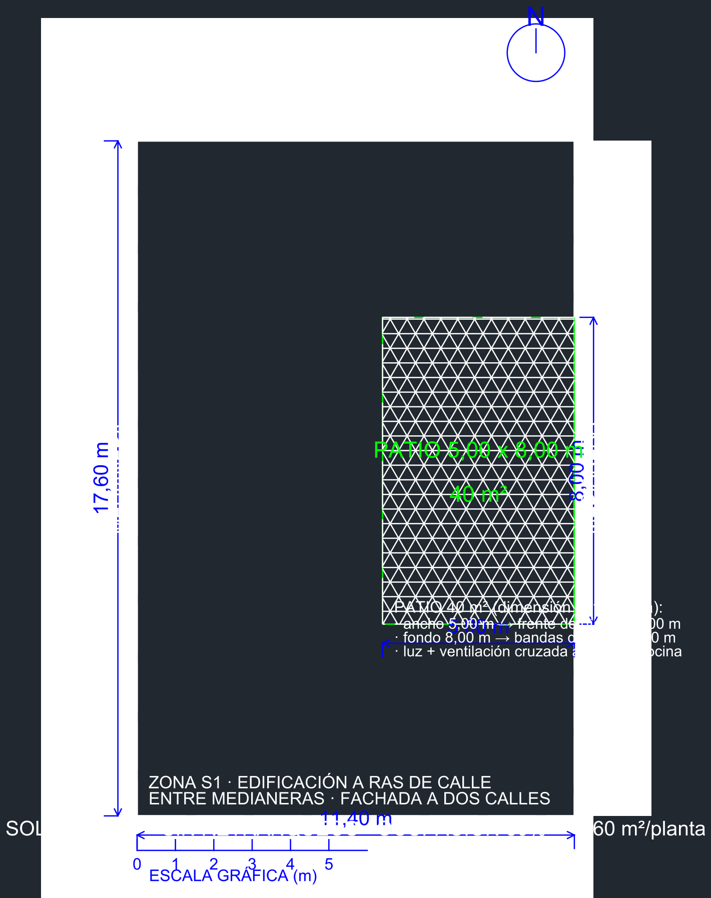
N
17,60 m
PATIO 5,00 x 8,00 m
40 m²
8,00
5,00 m
PATIO 40 m² (dimensión
):
ancho 5,00 m → frente de
00 m
· fondo 8,00 m → bandas d
0 m
· luz + ventilación cruzada a
ocina
ZONA S1 · EDIFICACIÓN A RAS DE CALLE
ENTRE MEDIANERAS · FACHADA A DOS CALLES
11,40 m
SOL
60 m²/planta
0
1
2
3
4
5
ESCALA GRÁFICA (m)

,40 m)

PLANO P-00 · SITUACIÓN E IMPLANTACIÓN

- PARCEL
- PATIO 40 m² (5 x 8) · lindero derecho
- HUELLA 80% = 160 m²/planta
- VIARIO (calles)
- MEDIANERA (linderos vecinos)
- COTAS / NORTE / ESCALA

v6.1 · COCINA JUNTO A ESCALERA Y SALÓN AMPLIADO:

- COCINA → FRENTE DERECHA (X 6,40–10,40), LINDANDO CON LA ESCALERA DE P.A.
- LA ANTIGUA COCINA SE INCORPORA AL SALÓN (X 1,40–6,40 × Y 0–7,40 = 37 m²)
- ÚNICA SEPARACIÓN COCINA–SALÓN: PUERTA CORREDERA DOBLE (ABIERTA = TODO UNIDO)
- COCINA Y SALÓN ABREN AL PORCHE · PORTAL VIV. B EN ESQUINA DERECHA
- PUERTAS DE ACCESO DESDE LA CALLE: PORTAL A Y PORTAL B · 1,00 m DE ANCHO

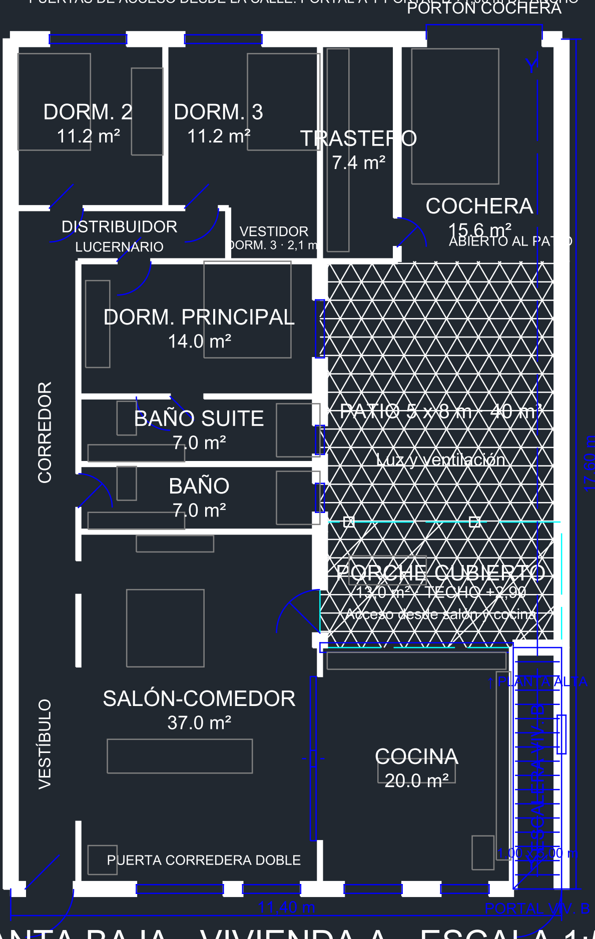
PORTÓN COCHERA
DORM. 2
11.2 m²
DORM. 3
11.2 m²
TRASTERO
7.4 m²
COCHERA
15.6 m²
ABIERTO AL PATIO
Y
DISTRIBUIDOR
LUCERNARIO
VESTIDOR
DORM. 3 · 2,1 m
DORM. PRINCIPAL
14.0 m²
PATIO 5 x 8 m · 40 m²
Luz y ventilación
17,60 m
CORREDOR
BAÑO SUITE
7.0 m²
BAÑO
7.0 m²
PORCHE CUBIERTO
13.0 m² · TECHO +2,90
Acceso desde salón y cocina
↑ PLANTA ALTA
SALÓN-COMEDOR
37.0 m²
VESTÍBULO
COCINA
20.0 m²
ESCALERA VIV. B
1,00 x 5,00 m
PUERTA CORREDERA DOBLE
11,40 m
PORTAL VIV. B

PLANTA BAJA · VIVIENDA A · ESCALA 1:50

CASA BIFAMILIAR · PALMA DEL RÍO · SOLAR 200 m² · S1

P-01 · PLANTA BAJA (VIVIENDA A) · v6.1 ESCALA 1:50

PLANTA ALTA · VIVIENDA B · v8 (GRAN SALÓN DIÁFANO 50 m²)

- v8 · SIN PARED SEPARADORA SALÓN-PASILLO: SALÓN AMPLIADO A 50 m² CORD. INTEGRADO
- v7 · DORM. 2 AL FONDO-DERECHA (23 m²) Y PATIO TRASERO ELEVADO PRIVADO (11,2 m²)
- ACCESO: ESCALERA RECTA INDEPENDIENTE DESDE PORTAL B A PLANTA ALTA
- CUBIERTA CERRADA Y TRANSITABLE SÓLO PARA MANTENIMIENTO (SIN ESCALERA AL TEJADO)
- FLUIDEZ TOTAL DE ILUMINACIÓN Y VENTILACIÓN EN TODAS LAS CARPINTERÍAS

INSTALACIONES

E	ELECTRICIDAD
F	FONTANERÍA
B	BAJANTES
S	SANEAMIENTO
C	CLIMATIZACIÓN
T	TELECOM

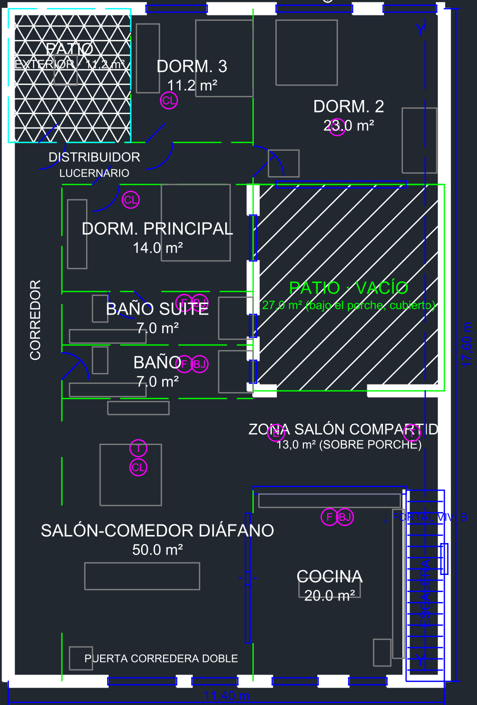
PATIO
EXTERIOR · 11,2 m²
DORM. 3
11.2 m²
CL
DORM. 2
23.0 m²
DISTRIBUIDOR
LUCERNARIO
CL
DORM. PRINCIPAL
14.0 m²
PATIO · VACÍO
27,0 m² (bajo el porche, cubierto)
CORREDOR
BAÑO SUITE
7.0 m²
F
BJ
BAÑO
7.0 m²
F
BJ
ZONA SALÓN COMPARTID
13,0 m² (SOBRE PORCHE)
E
T
T
CL
F
BJ
↓ PORTAL VIV. B
SALÓN-COMEDOR DIÁFANO
50.0 m²
COCINA
20.0 m²
ESCALERA
PUERTA CORREDERA DOBLE
17,60 m
11,40 m

PLANTA ALTA · VIVIENDA B · EN BRUTO · ESCALA 1:50

CASA BIFAMILIAR · PALMA DEL RÍO · SOLAR 200 m² · S1
P-02 · PLANTA ALTA (VIVIENDA B) · v7 ESCALA 1:50

ALZADOS Y SECCIÓN · ESCALA 1:100

SECCIÓN Y-Y · X = 10,90 (ESCALERA / PORCHE / PATIO / DORM. 2)

ALZADO PRINCIPAL · C/ MORENO TORROBA

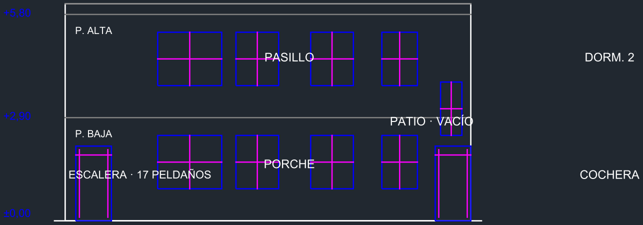
+5,80
P. ALTA
PASILLO
DORM. 2
+2,90
PATIO · VACÍO
P. BAJA
PORCHE
ESCALERA · 17 PELDAÑOS
COCHERA
±0,00

ALZADO TRASERO · CALLE TRASERA

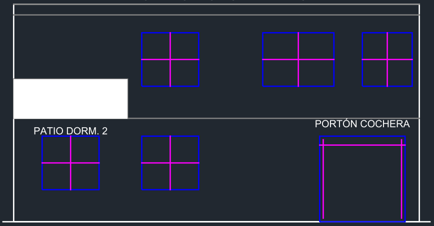
PORTÓN COCHERA
PATIO DORM. 2

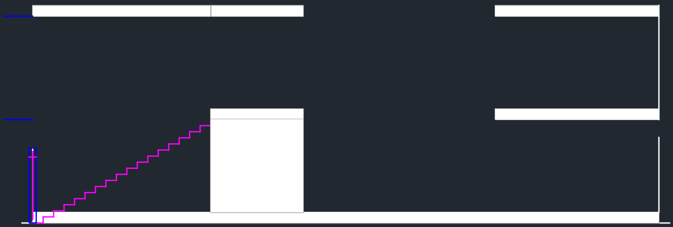

CASA BIFAMILIAR · PALMA DEL RÍO · SOLAR 200 m² · S1

P-03/P-04 · ALZADOS + SECCIÓN · v1

ESCALA 1:100m

CUADRO DE SUPERFICIES · CASA BIFAMILIAR

PALMA DEL RÍO (CÓRDOBA) · SOLAR 200 m² · OCUPACIÓN 80 % (160 m²/planta)

ESTANCIA	SUP. (m²)	REF.
PLANTA BAJA · VIVIENDA A (P-01)		
Salón-comedor	37.0	A1
Cocina	20.0	A2
Vestíbulo	8.3	A3
Corredor	9.9	A4
Baño	7.0	A5
Baño suite	7.0	A6
Dorm. principal	14.0	A7
Distribuidor	5.0	A8
Vestidor dorm3	2.1	A9
Dorm. 2	11.2	A10
Dorm. 3	11.2	A11
Trastero	7.4	A12
Cochera	15.6	A13
SUBTOTAL ÚTIL P-01	155.7	A
PLANTA ALTA · VIVIENDA B (P-02)		
Salón-comedor diáfano (inc. pasillo)	50.0	B1
Cocina	20.0	B2
Corredor	9.9	B3
Baño	7.0	B4
Baño suite	7.0	B5
Dorm. principal	14.0	B6
Distribuidor	7.0	B7
Dorm. 2 (sobre cochera)	23.0	B8
Dorm. 3	11.2	B9
SUBTOTAL ÚTIL P-02	149.1	B
EXTERIORES		
Patio planta baja	40.0	
Porche cubierto	13.0	
Patio trasero planta alta	11.2	
Vacío patio (no construido)	27.0	

RESUMEN

Superficie construida P-01 (Vivienda A): 160,0 m² (80 % del solar)

Superficie construida P-02 (Vivienda B): 133,0 m² (sin el vacío del patio)

Superficie útil total (A + B): 304,8 m²

Total construido: 293,0 m²

PRESUPUESTO ORIENTATIVO (construcción, sin urbanización ni honorarios)

293 m² × 1.300 €/m² ≈ 381.000 € (rango estimado 350.000 – 420.000 €)

Incluye: obra gruesa, cubierta, carpintería exterior, instalaciones básicas y acabados estándar.

CASA BIFAMILIAR · PALMA DEL RÍO · SOLAR 200 m² · S1
P-05 · CUADRO DE SUPERFICIES · v1 ESCALA —