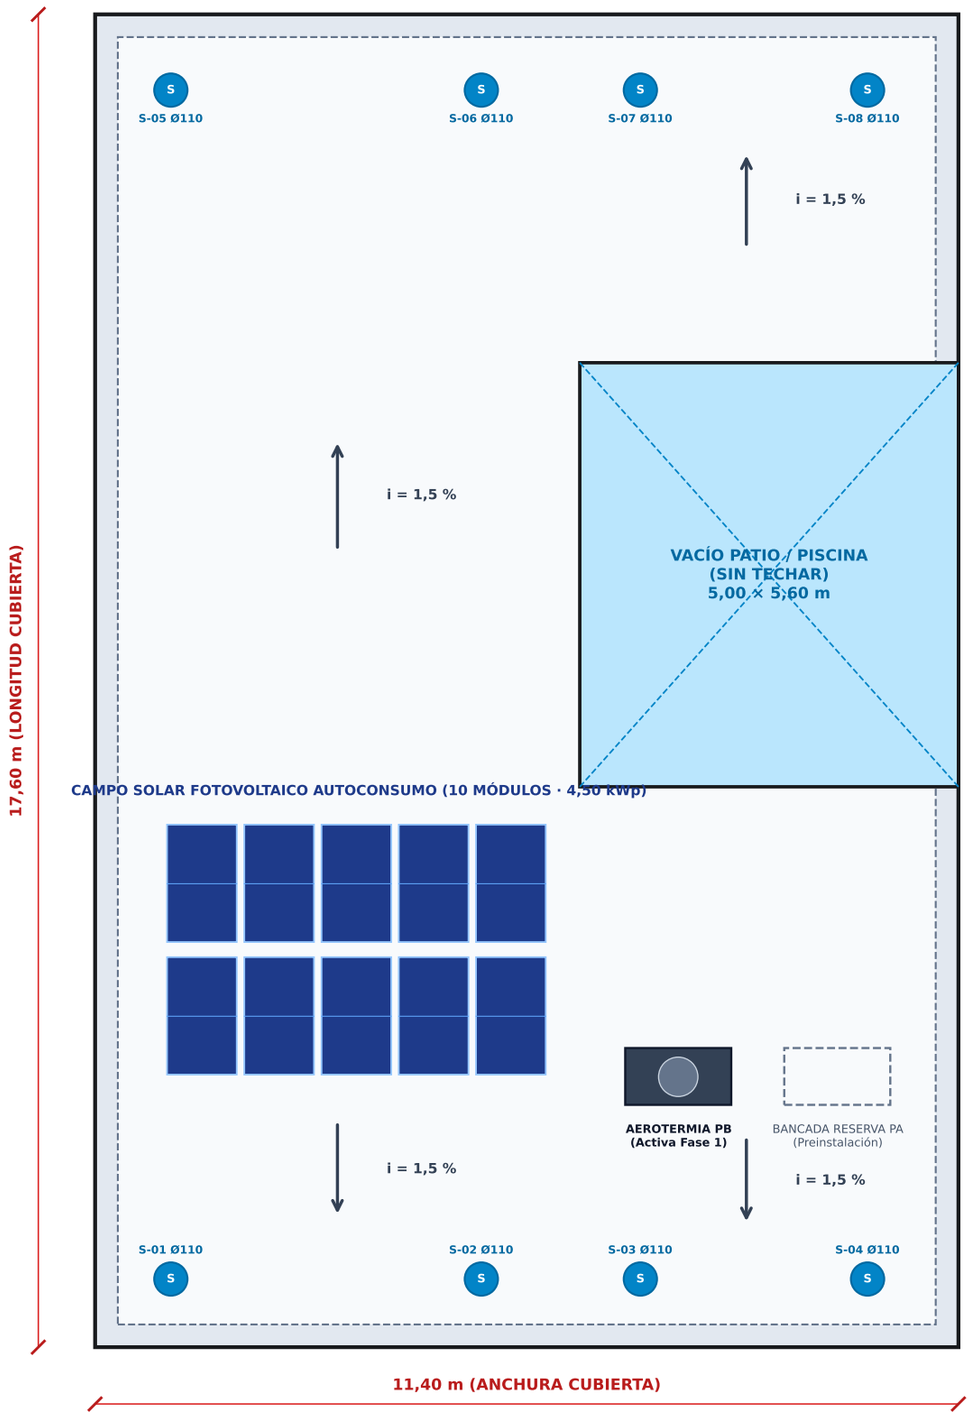

PROYECTO BÁSICO Y DE EJECUCIÓN Vivienda Unifamiliar en PB + Espacio en Bruto en PA **Calle Moreno Torroba s/n · Palma del Río (Córdoba)**	**PLANO: PLANTA DE CUBIERTAS E INSTALACIONES** Cubierta Plana Invertida (XPS 100 mm), Sumideros Sifónicos, Aerotermia y Fotovoltaica **Documento Reglamentario CTE · Solicitud Licencia de Obras**	**ESCALA: 1:100** FECHA: Octubre 2026 FORMATO: DIN A3	PLANO Nº **P-03**